



DESIGN PORTFOLIO
PARKER MURPHY

PROJECT 1

EARTH-AIR PLANTHOUSE

PARADISE VALLEY, MT


INTENSIVE FOCUS ON SYSTEMS THINKING AND THE
REAL- WORLD APPLICATION OF SUSTAINABLE
DESIGN

This project was extremely site- focused and
involved a plethora of analysis, including
watershed patterns, subsurface earth
temperatures, sun trajectory and snow-load.

PERMENANCE AND TRANSIENCE

AGROUNDED MASS NESTS THIS SANCTUARY IN THE HILLSIDE,
CONTRASTED BY THE DELACATE GROWTH OF SOFT GLAZING




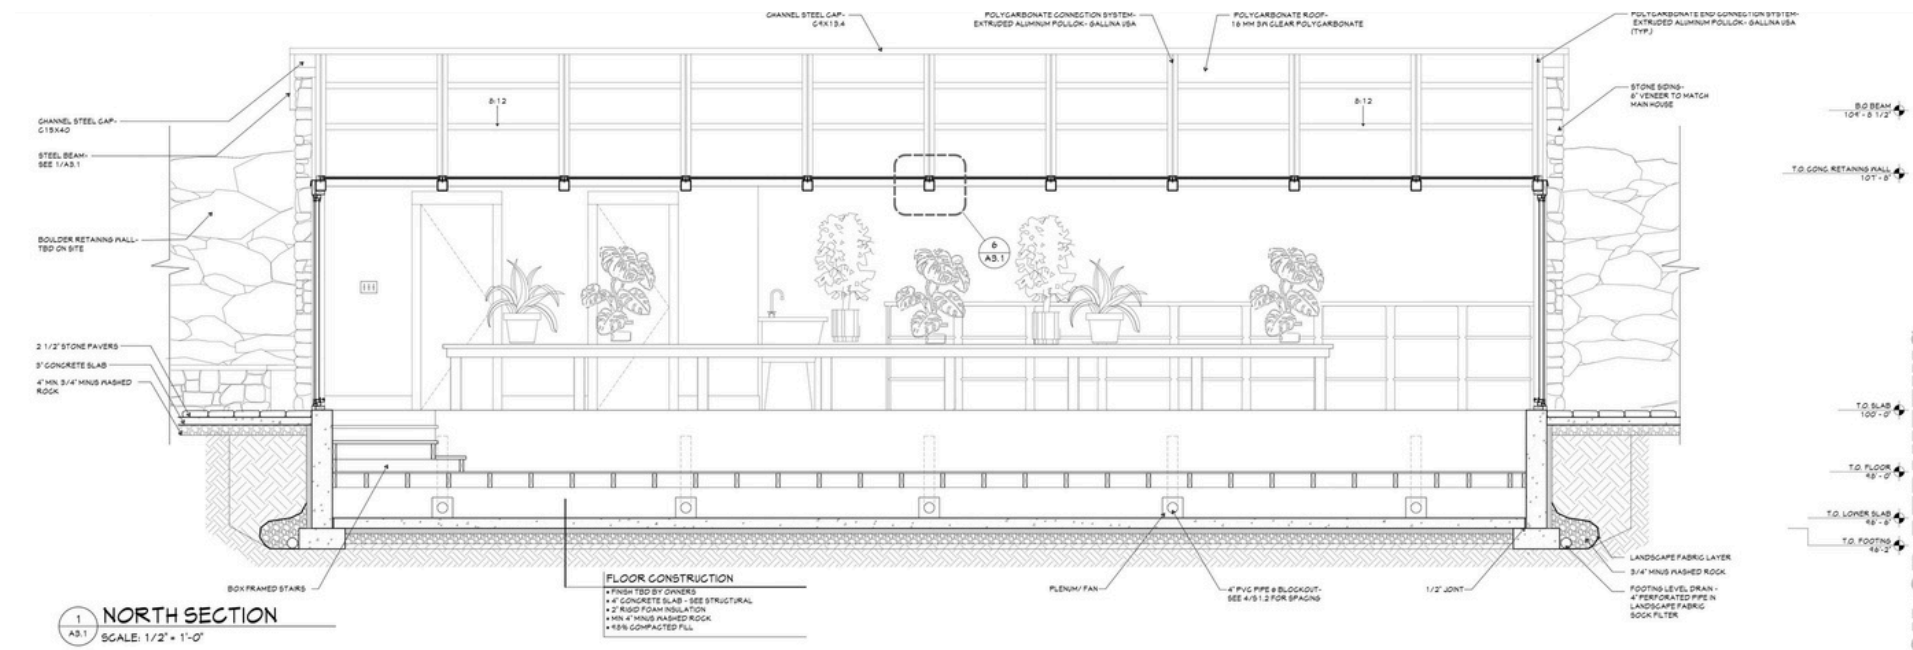

ELEVATION STUDY

VISIBLY CLEARDESIGN DICHOTOMY

Further design development reflected the building relationship to the land and its composing pieces.

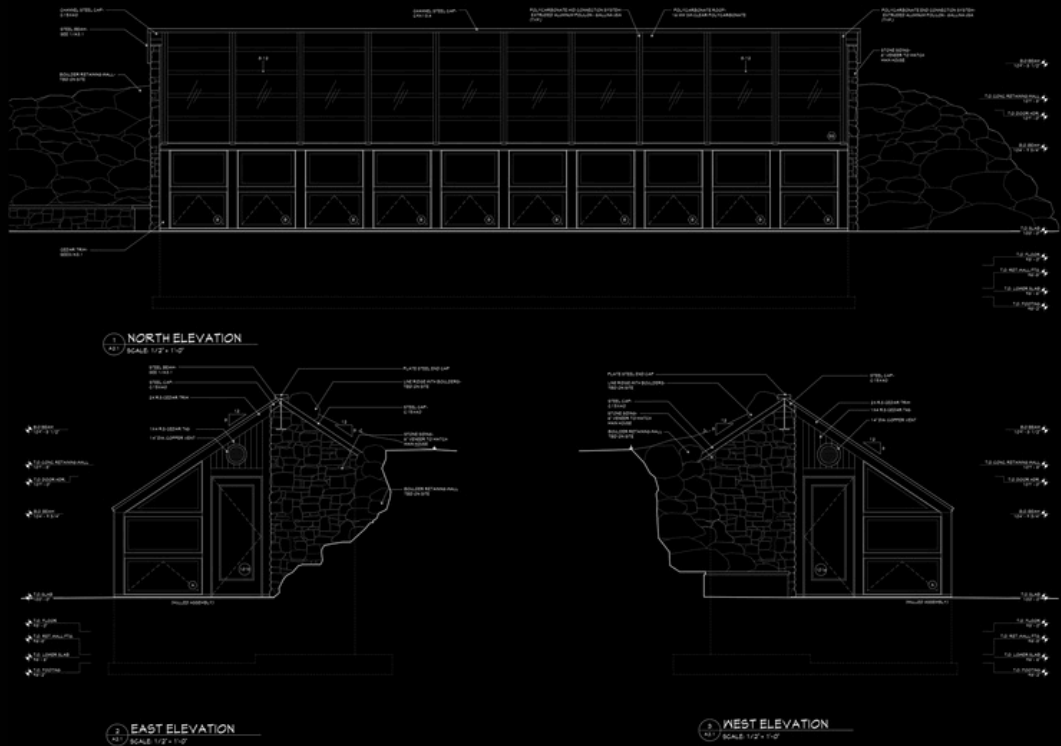

PROPORTION/ RHYTHM

BLURRING LINES BETWEEN BUILT SPACE AND THE LANDSCAPE


A delicate glazed system rests on a steel spine with HSS rib purlins providing functionality and rhythm.



STRUCTURAL DESIGN

FOUNDATION AND DRAINAGE DESIGN

Quality drafting and clear representation of foundation sizes, spacing and requirements is imperative for an accurate product.

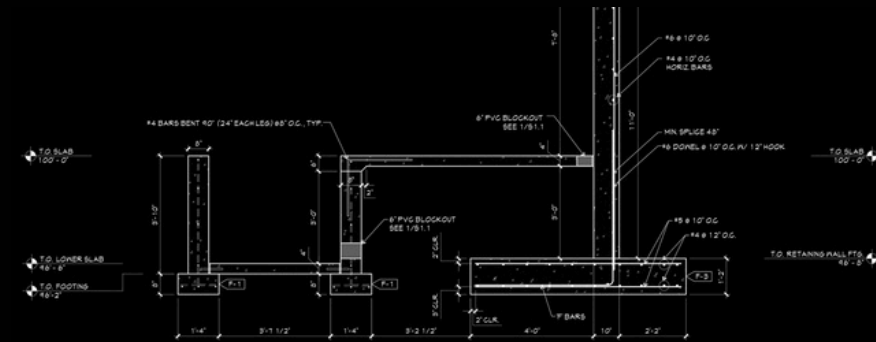


2 CONCRETE DETAIL SECTION
91.1 SCALE: 1/2" = 1'-0"

1 FOUNDATION PLAN
91.1 SCALE: 1/2" = 1'-0"

BUILDING COMPOSITION


CONNECTIONS AND WATERPROOFING

Designing structural connections that aligned with the project abstract while supporting heavy snow loads. Creative solutions using mixed- material design.

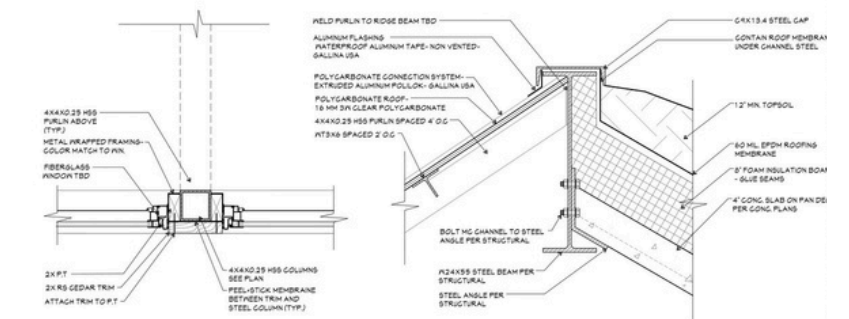


9 STEEL COLUMN DETAIL
A3.1 SCALE: 1 1/2" = 1'-0"

4 RIDGE DETAIL
A3.1 SCALE: 1 1/2" = 1'-0"

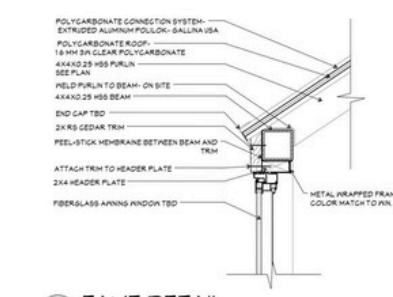

5 EAVE DETAIL
A3.1 SCALE: 1 1/2" = 1'-0"

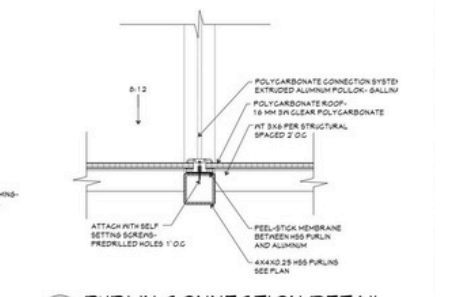

6 PURLIN CONNECTION DETAIL
A3.1 SCALE: 1 1/2" = 1'-0"

PROJECT 2

POWERS RESIDENCE

LIVINGSTON, MT

FOCUS ON CLEAN LINES AND RELATIONSHIPS IN THE CRAFTSMAN DESIGN STYLE

This is a current project and my first as a lead member of the design team. My design focusses on client wants, using traditional craftsman style architecture as precedent to create a “bungalow” style oasis.


CRAFTSMAN STYLE BUNGALOW

DESIGNING A FAMILY HOME WITH A DETAIL ORIENTED MINDSET. CLEAN LINES, BIBLICAL REFERENCE AND A SYSTEMIC APPROACH TO BUILT RELATIONSHIPS




SITE CONDITIONS

DEFINING A FOOTPRINT BASED AROUND RESIDENTIAL CODE AND FOCUSSED VIEWPOINTS
Designing in a growing urban environment requires maximized spacial use based on the program.

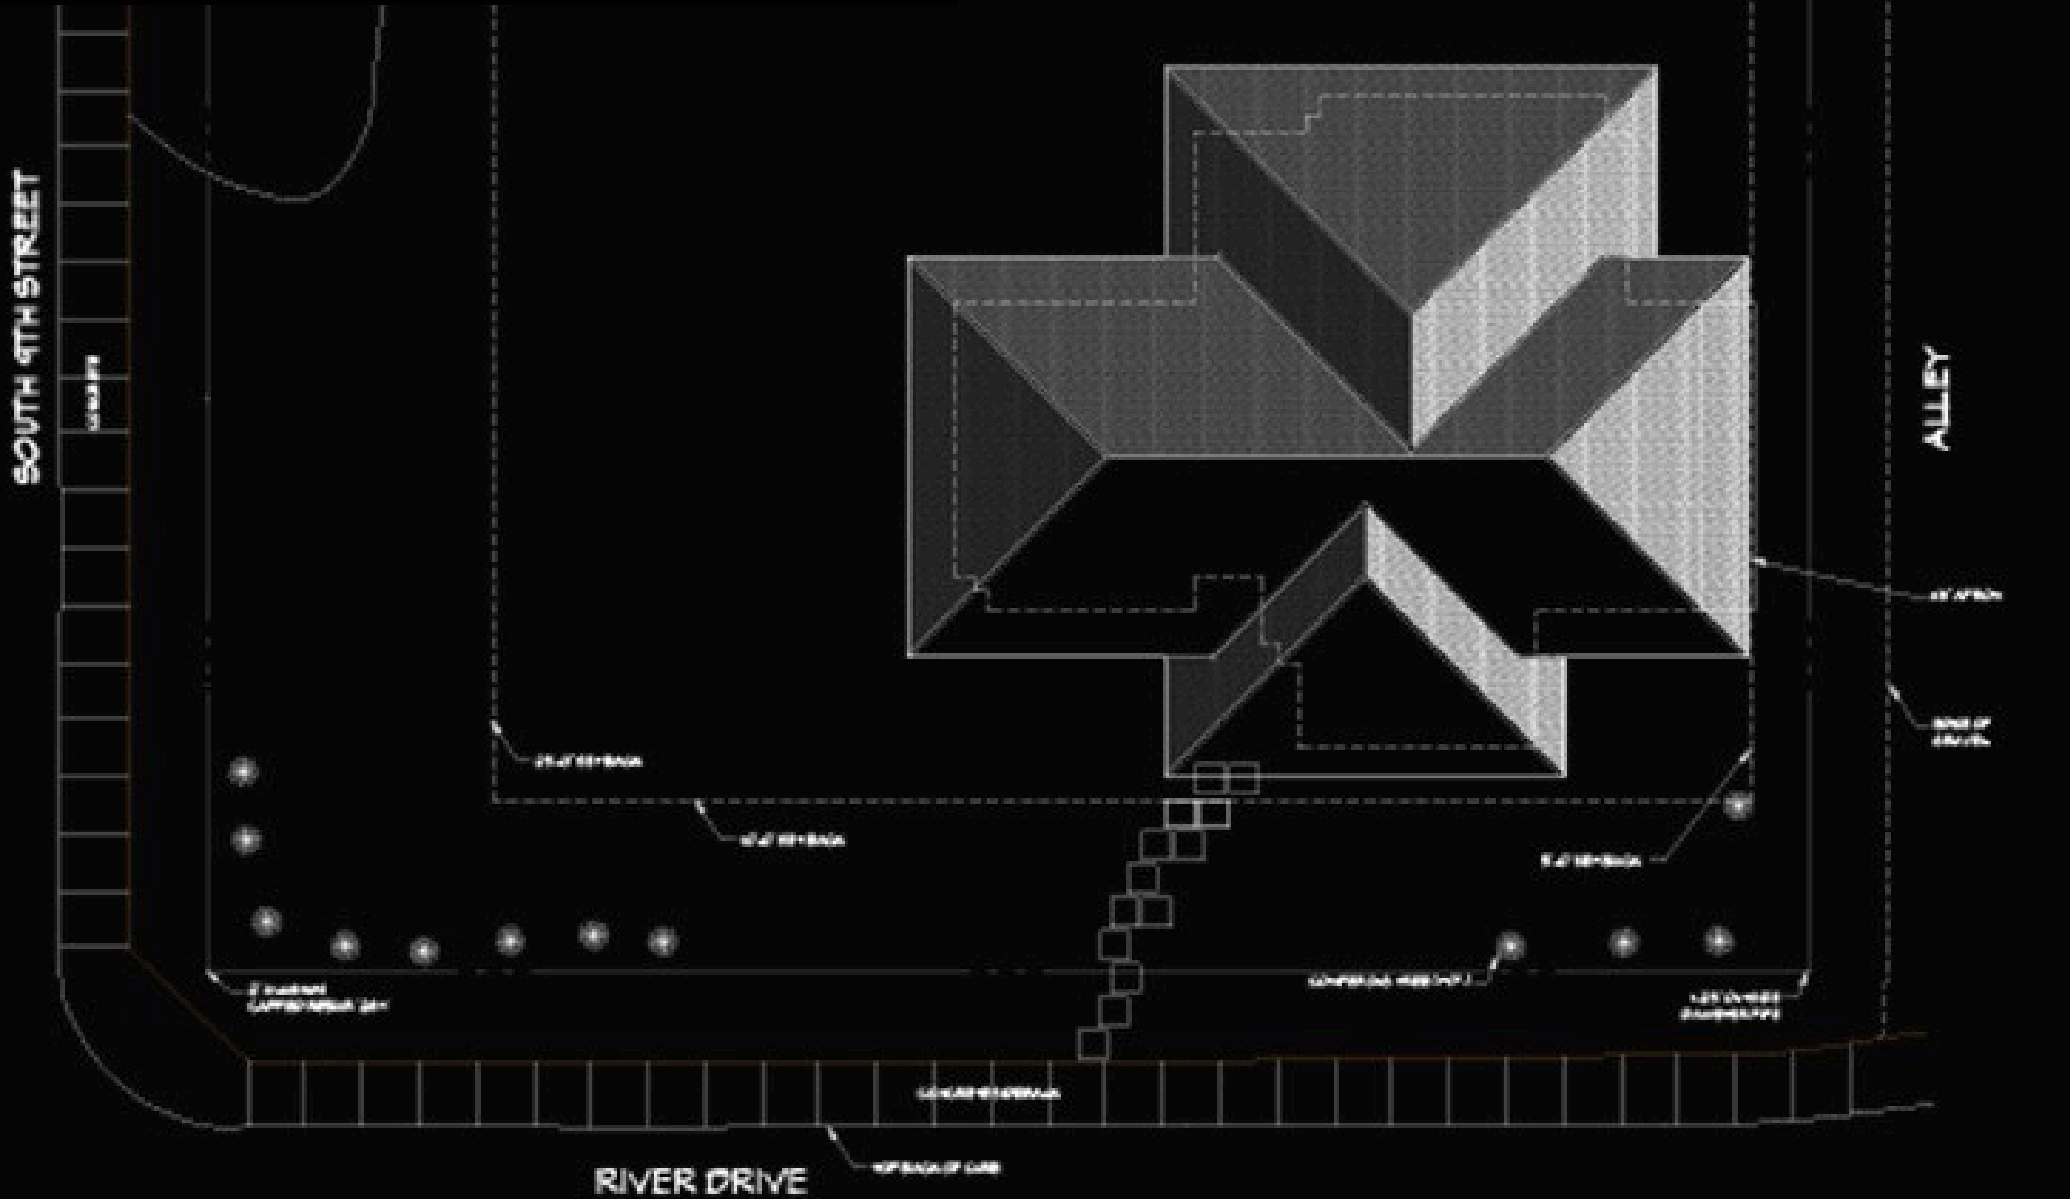

DESIGN LAYOUT

STUDYING ANGLES AND SPACE PLANNING
Biblical reference to the holy Trinity results in the inclusion of “threes”. Tri-pointed angles and large overhangs reflect this concept. Practical design plays an important role when designing within a budget. This project makes use of the client wants/needs to create a truly custom floorplan.

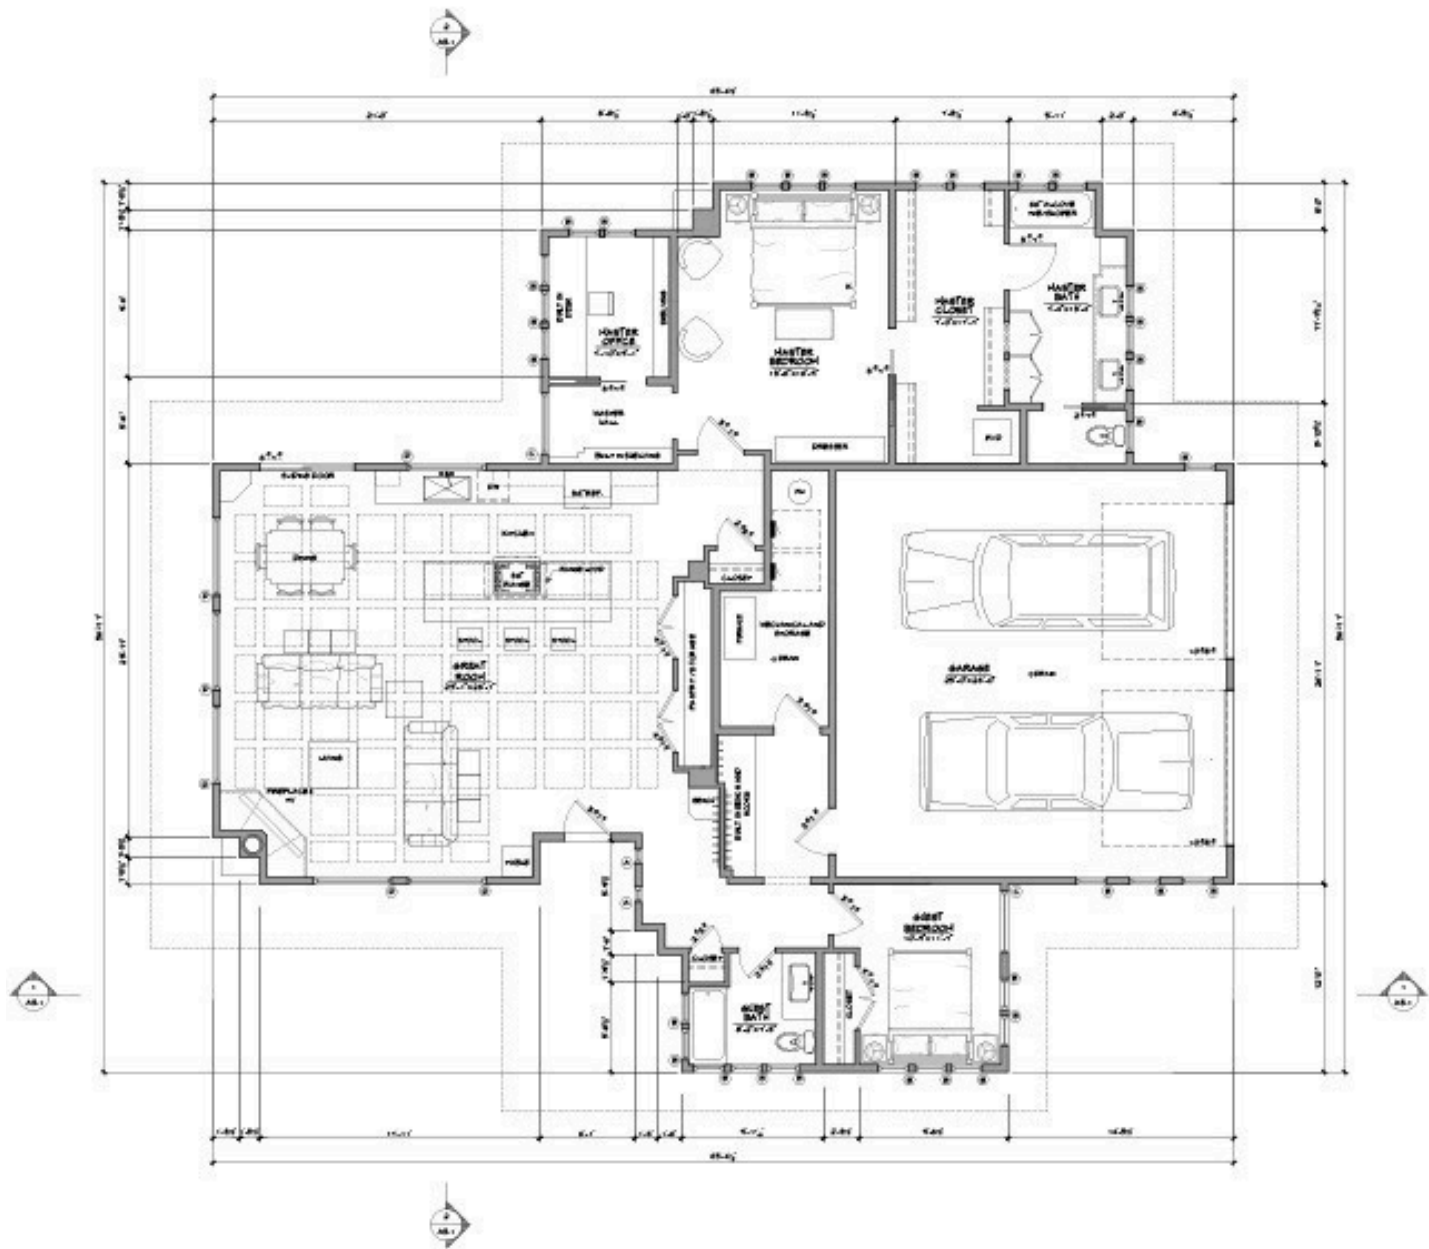

DRAFTED IN AUTOCAD

GLAZING

WINDOW SIZING AND PLACEMENT

Square shaped windows adhere to the idea of “uniformity” and “purity” mentioned in the old testament of the Bible. This causes resolve in the user experience of the space.



SKETCHUP MODELED BUILDING STUDY

MATERIAL USE


APPEALING REPETITION OF COLOR AND SIZING

The human eye looks for repetition and resolve in architecture. My design uses simple materials with thoughtful sizing to accomplish a cohesive exterior.




SECTIONS

REAL-WORLD APPLICATION OF BUILDING CONSTRUCTION
Section drawings defined the relationships between materials, window conditions and rooflines.

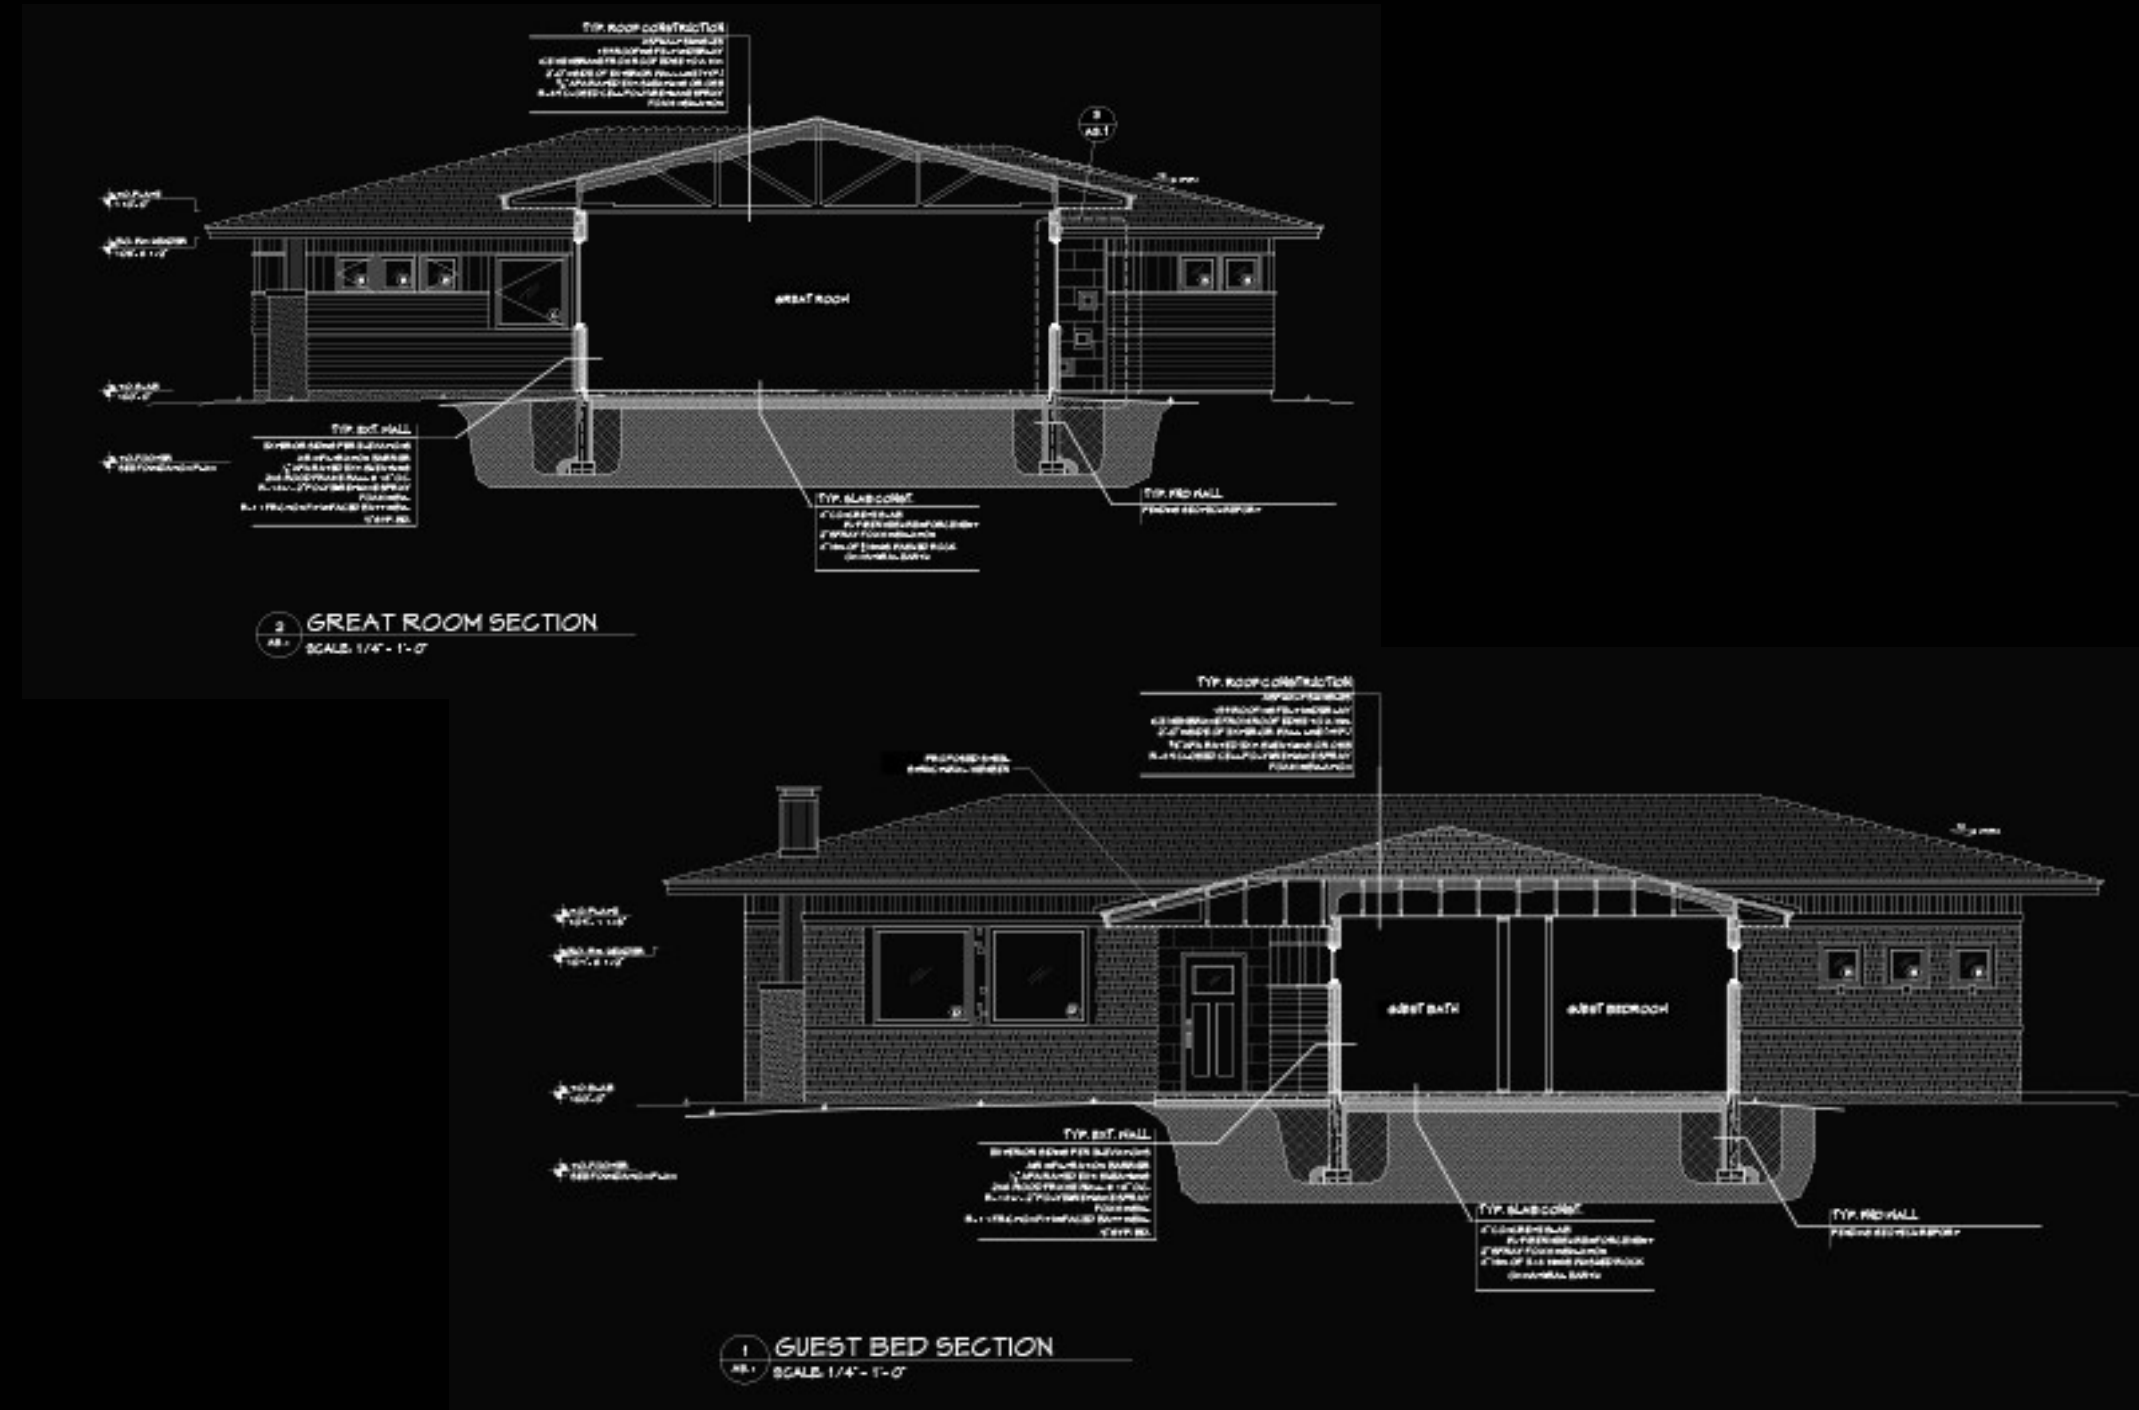

ELEVATIONS

FURTHER STUDYING BUILT RELATIONSHIPS
Using elevation views was the final step in design approval. Trim and eave banding around the exterior exemplify the abstract for this design

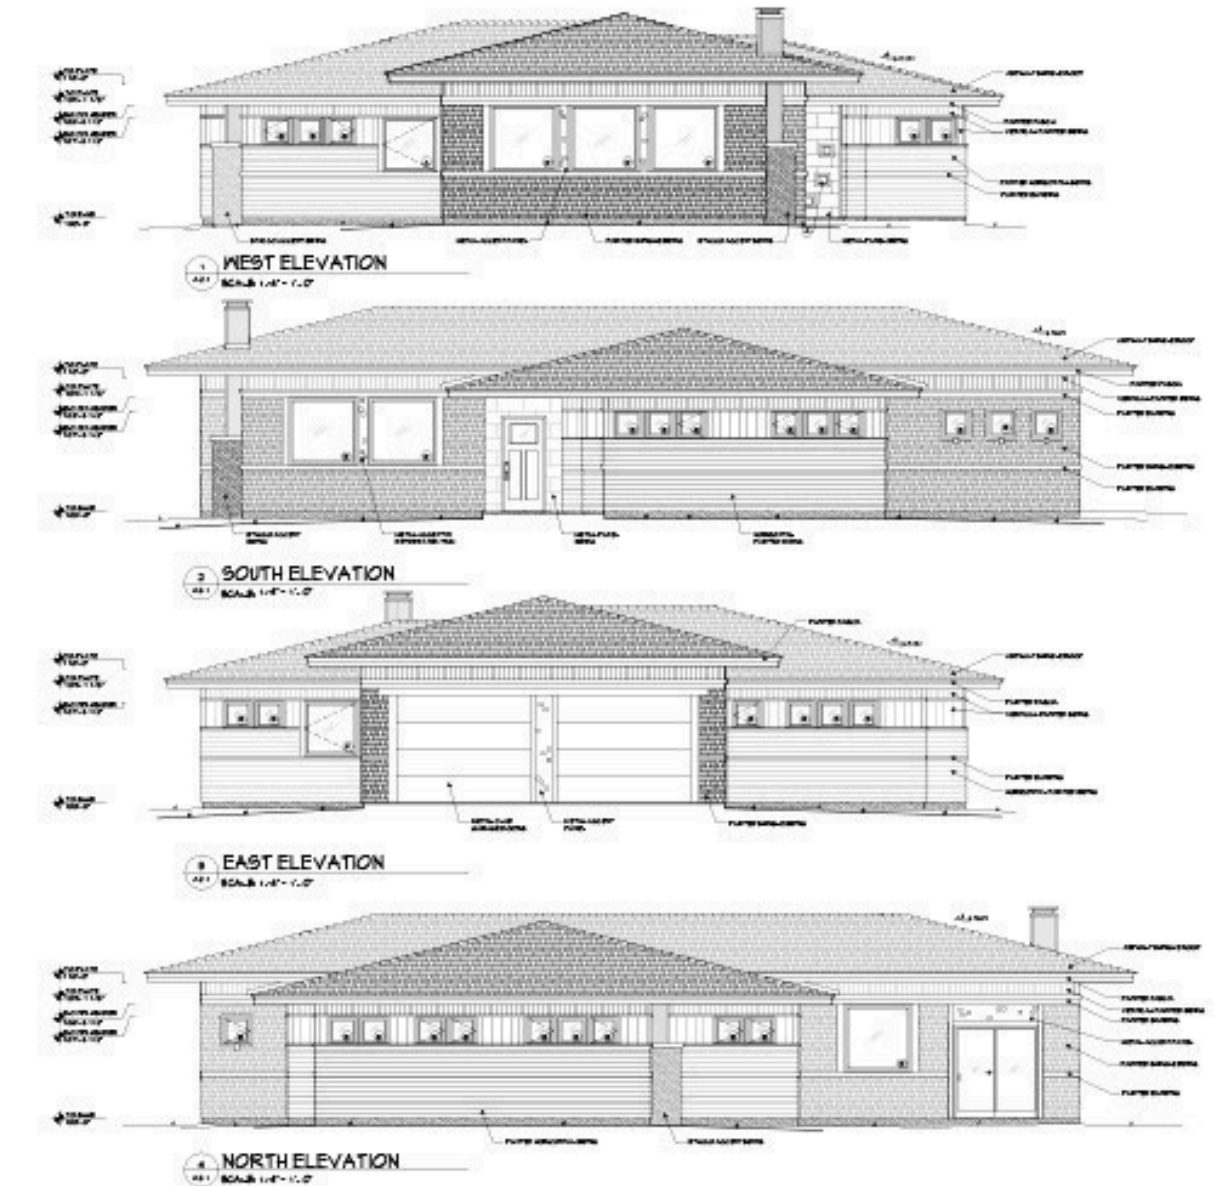


PROJECT 3

MUSEUM OF THE BEARTOOTHES NYE, MT

PROJECT FOCUS IN CULTURE AND WESTER HISTORY AS WELL AS MIXED MEDIA PRESENTATION METHODS
This project involved a difficult site that was rooted in Native American Culture and the history of the "Bison Jump". I explored both physical, digital and abstract methods of presentation and building development.

LANDSCAPE, LIGHT, MATERIALITY

DEVELOPING A CONNECTION BETWEEN HUMANS AND OUR ETHEREAL REACTION TO NATURE, LIGHT PATTERNS, AND BUILT SPACE

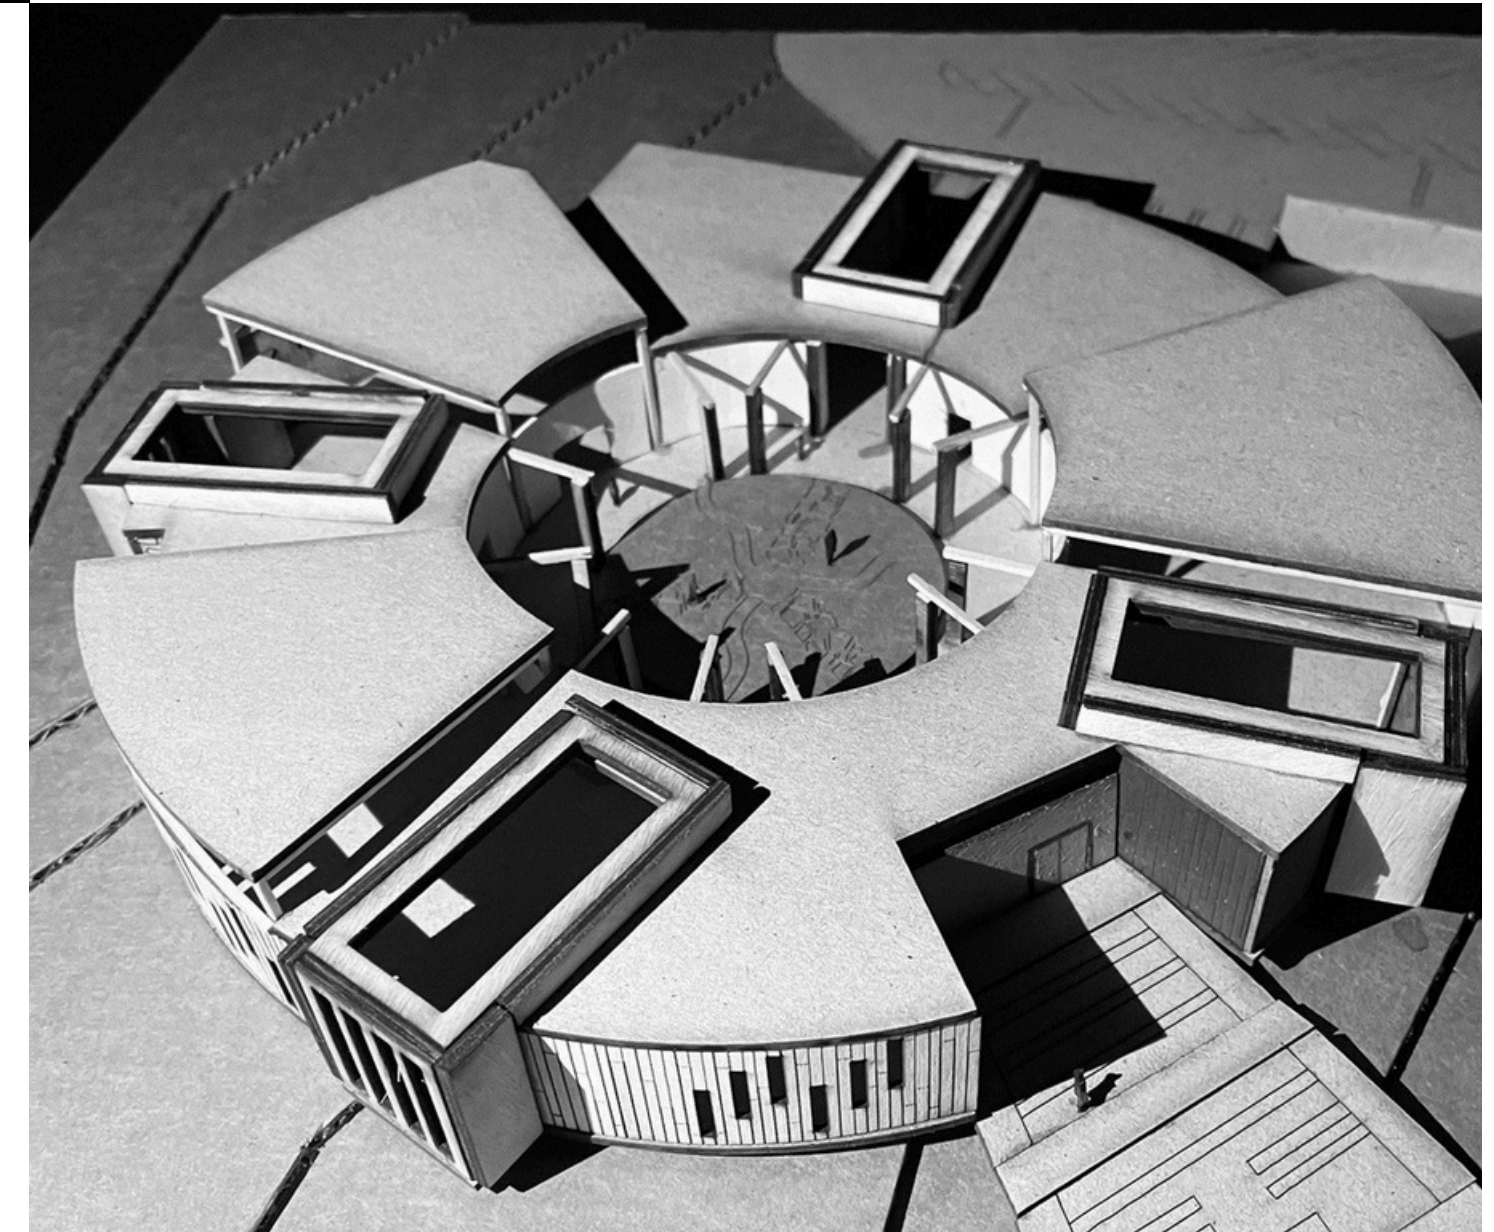

INTEGRATIVE DESIGN

STUDYING DEEP ROOTED CULTURAL HISTORY


Design process included research into the culture and presence of Native Americans on the site.



FORCE ANALYSIS

STUDYING NATURAL AND CULTURAL FORCES ON THE SITE


Site visits, historical records, eco- logical files, topographical maps and more aided to in the full under- standing of the forces present. Chart and natural forces that make the site unique. Using a combination of digital and physical methods of pre- sentation allowed me to graphically conditions

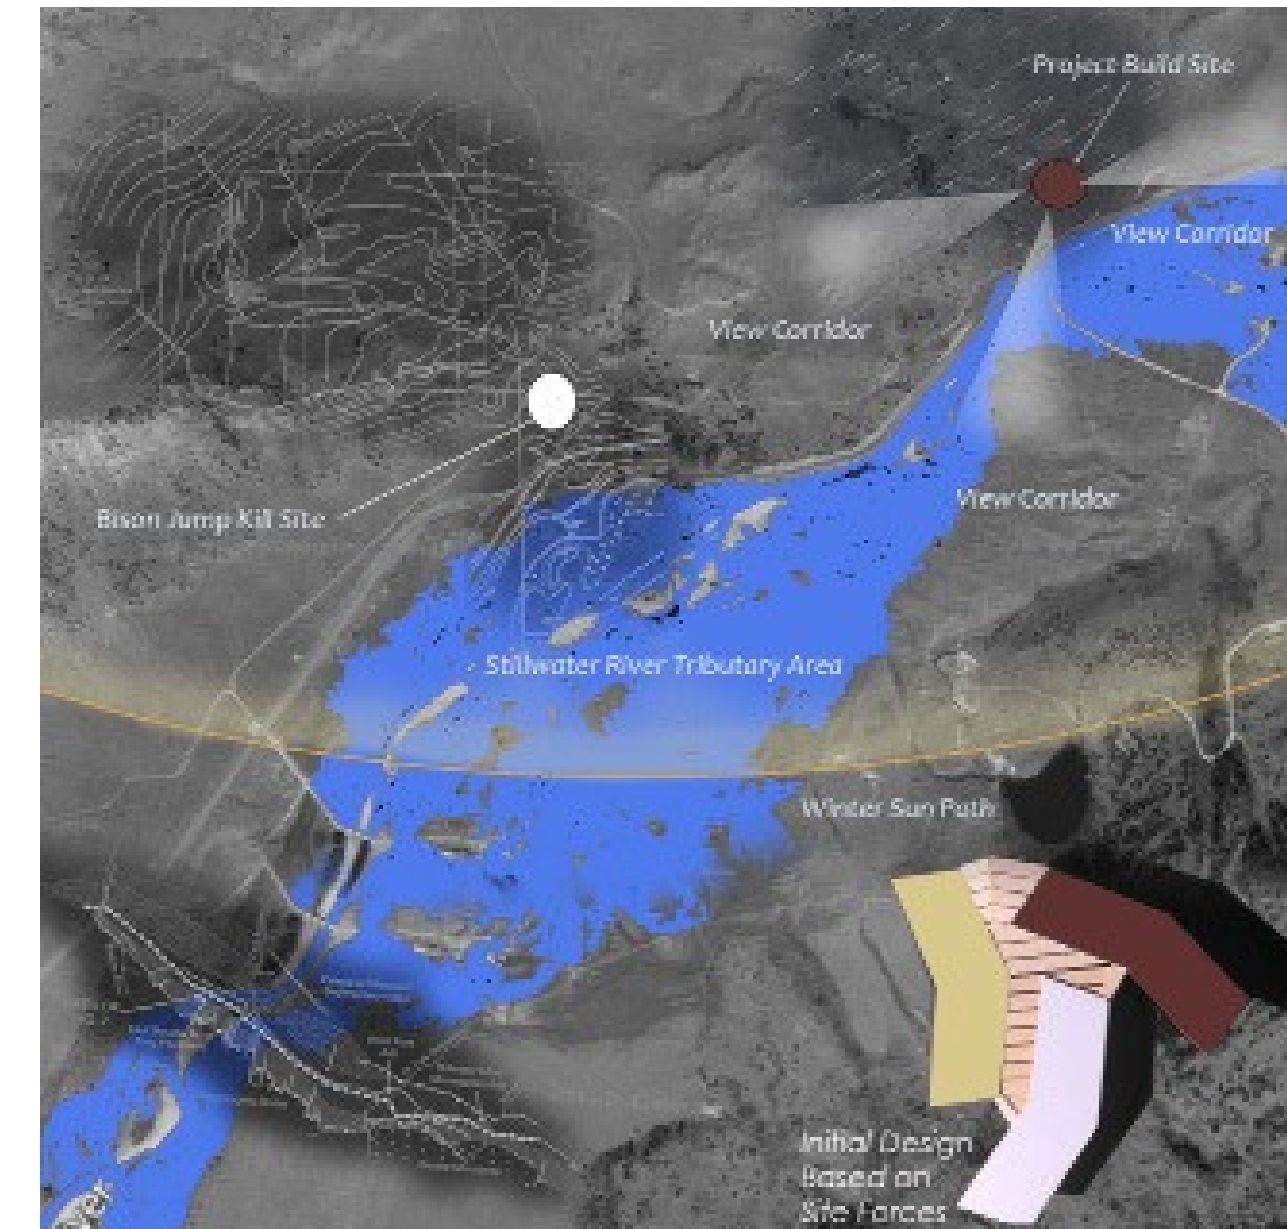

DIRECTIONALITY

USING THE LAND RATHER THAN UNEARTHING IT


Taking into account the natural site forces, my design involved a radial geometry that has "breaks", directing veiws to specific cultural factors and historic landmarks.

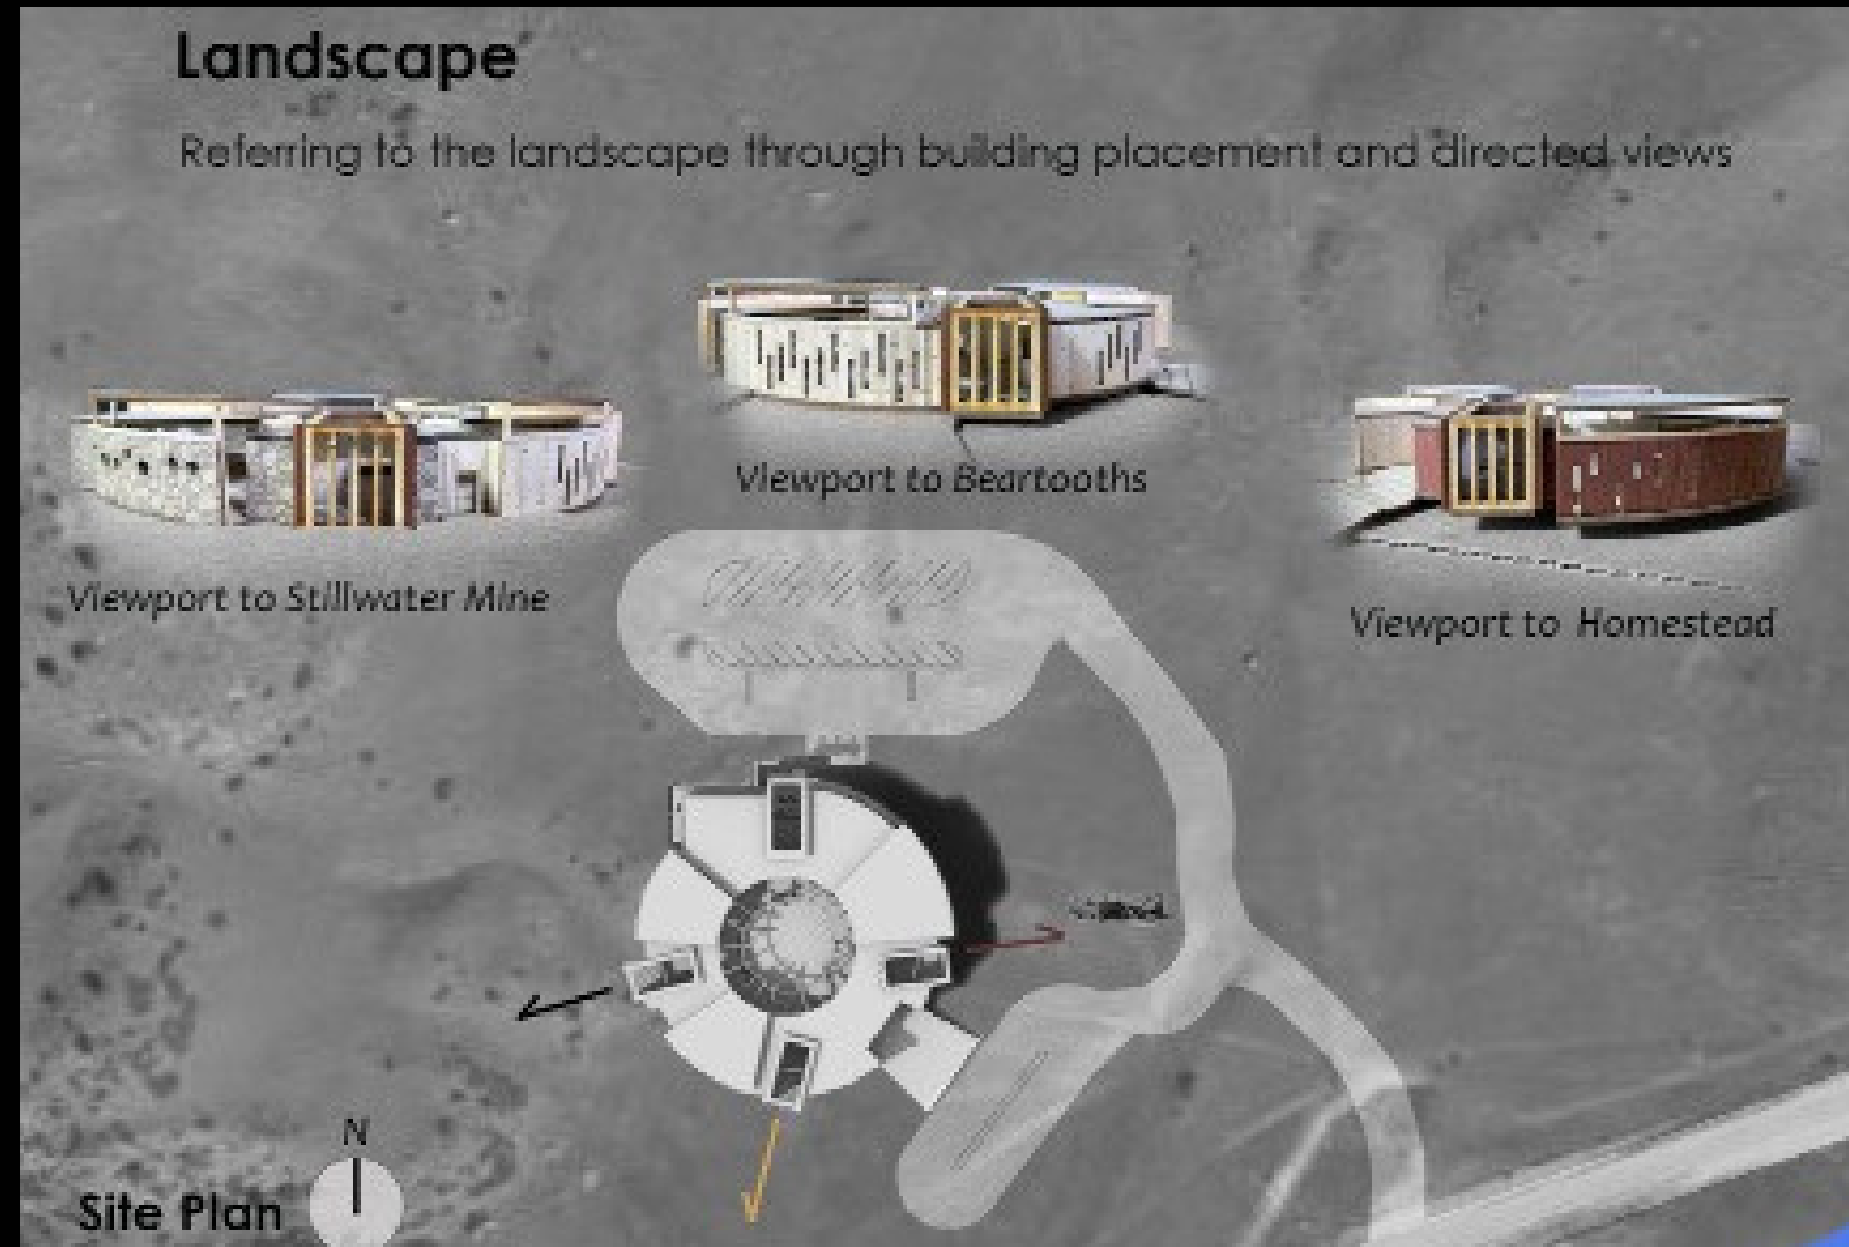

SACRED SYMBOLISM

IMPORTANCE OF THE CARDINAL DIRECTIONS AND THE MEDICINE WHEEL IN FIRST NATIONS HISTORY

The building footprint, along with the the sacred medicine wheel, a symbol which represented spirituality and self reflectance in plains indian cul- ture. The spaces span from a central courtyard, drawing veiwer's eyes "upward and outward". The organi- zation is aligned with Native Amer- icans connection to the earth and the sky, drawing users to have an emotional experience with each.

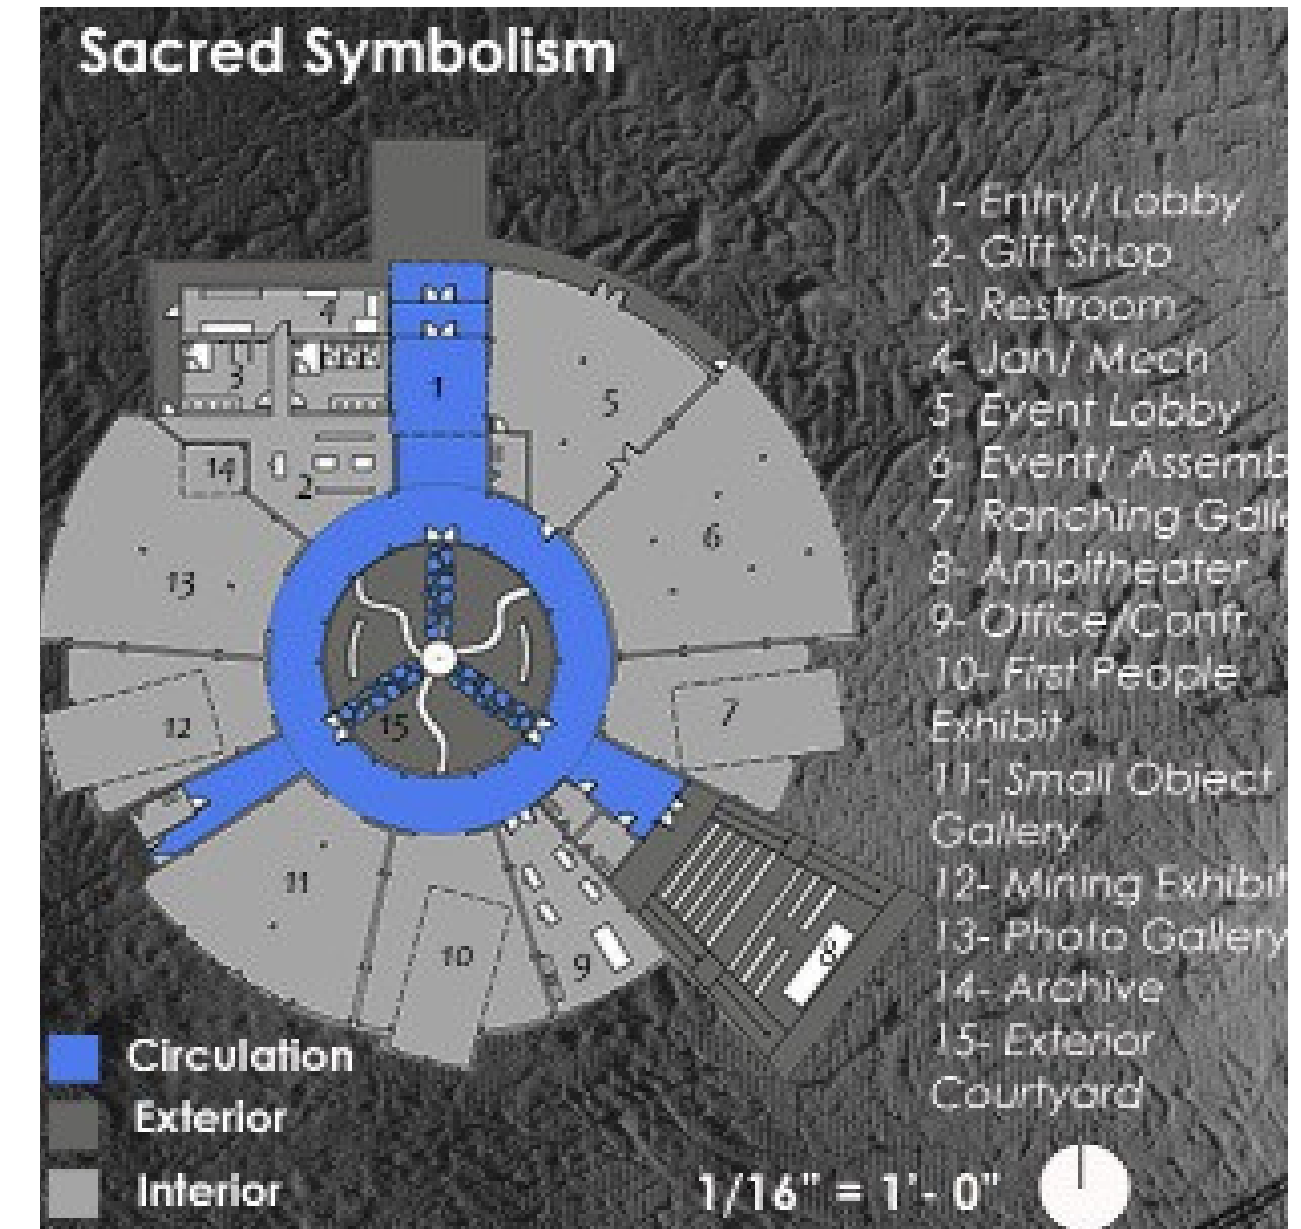


PHOTOSHOP/ RHINO 3D CREATED PLAN VIEWS

STRUCTURE

REFERRING TO CODE WITHIN A COMPLEX MAKEUP

Involving curves in architecture was often a task I wanted to attempt. Within that I had to learn code concepts in the form of load, occupancy, ect, which impacted my structural design solution.

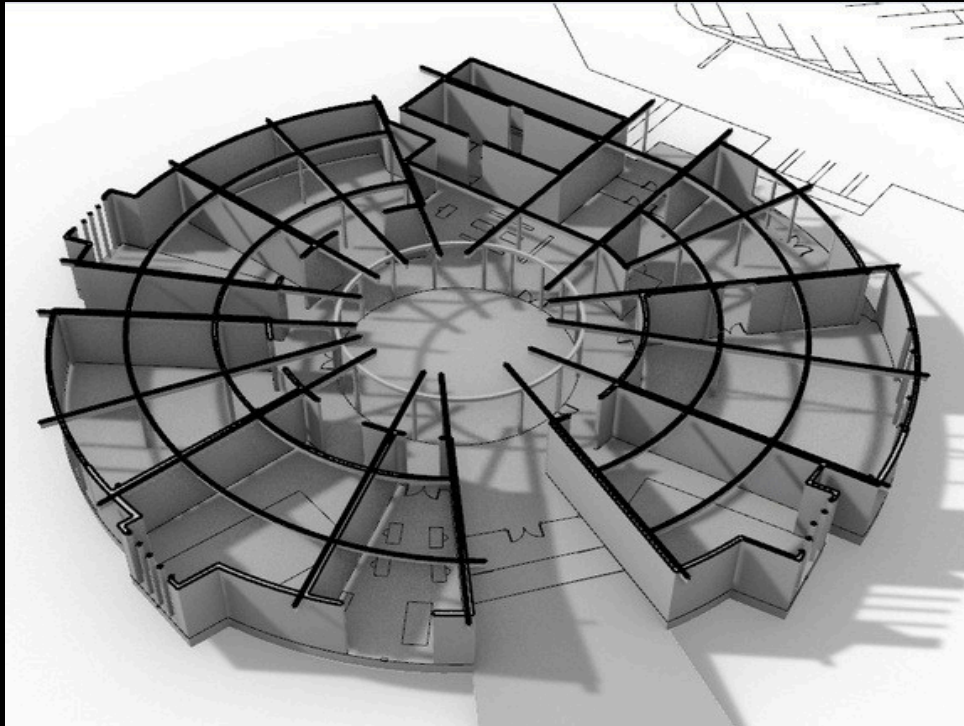

RHINO 3D MODELED STRUCTURE/ MASSING PLAN

MATERIALITY

REFLECTIVE OF VERNACULAR ARCHITECTURE

Using locally sourced, natural materials played an important role in designing an integrative yet creative building form- Representing a history of development in southwestern Montana.



HAND- BUILT MODEL



LIGHT OFFERINGS

CREATING CONNECTIONS THROUGH QUALITIES OF NATURAL LIGHT OFFERED IN UNIQUE WAYS

Furthering the user's connection the the sky, my design incorporated clerestory windows and large skylights. The exposed structural system imitates a "sun-dial", casting shadows depending on time of day and the season.

FILTRATION

FUNCTIONALITY AND BEAUTY FOR GALLERIES
Over the gallery spaces, large sky lights offer ample daylighting for displays, but serve as too direct in their shadowing. To combat this, I developed a light filtration system, made of semi-translucent material, so not only soften the light entering gallery spaces, but as a means to draw the eye upwards.

